



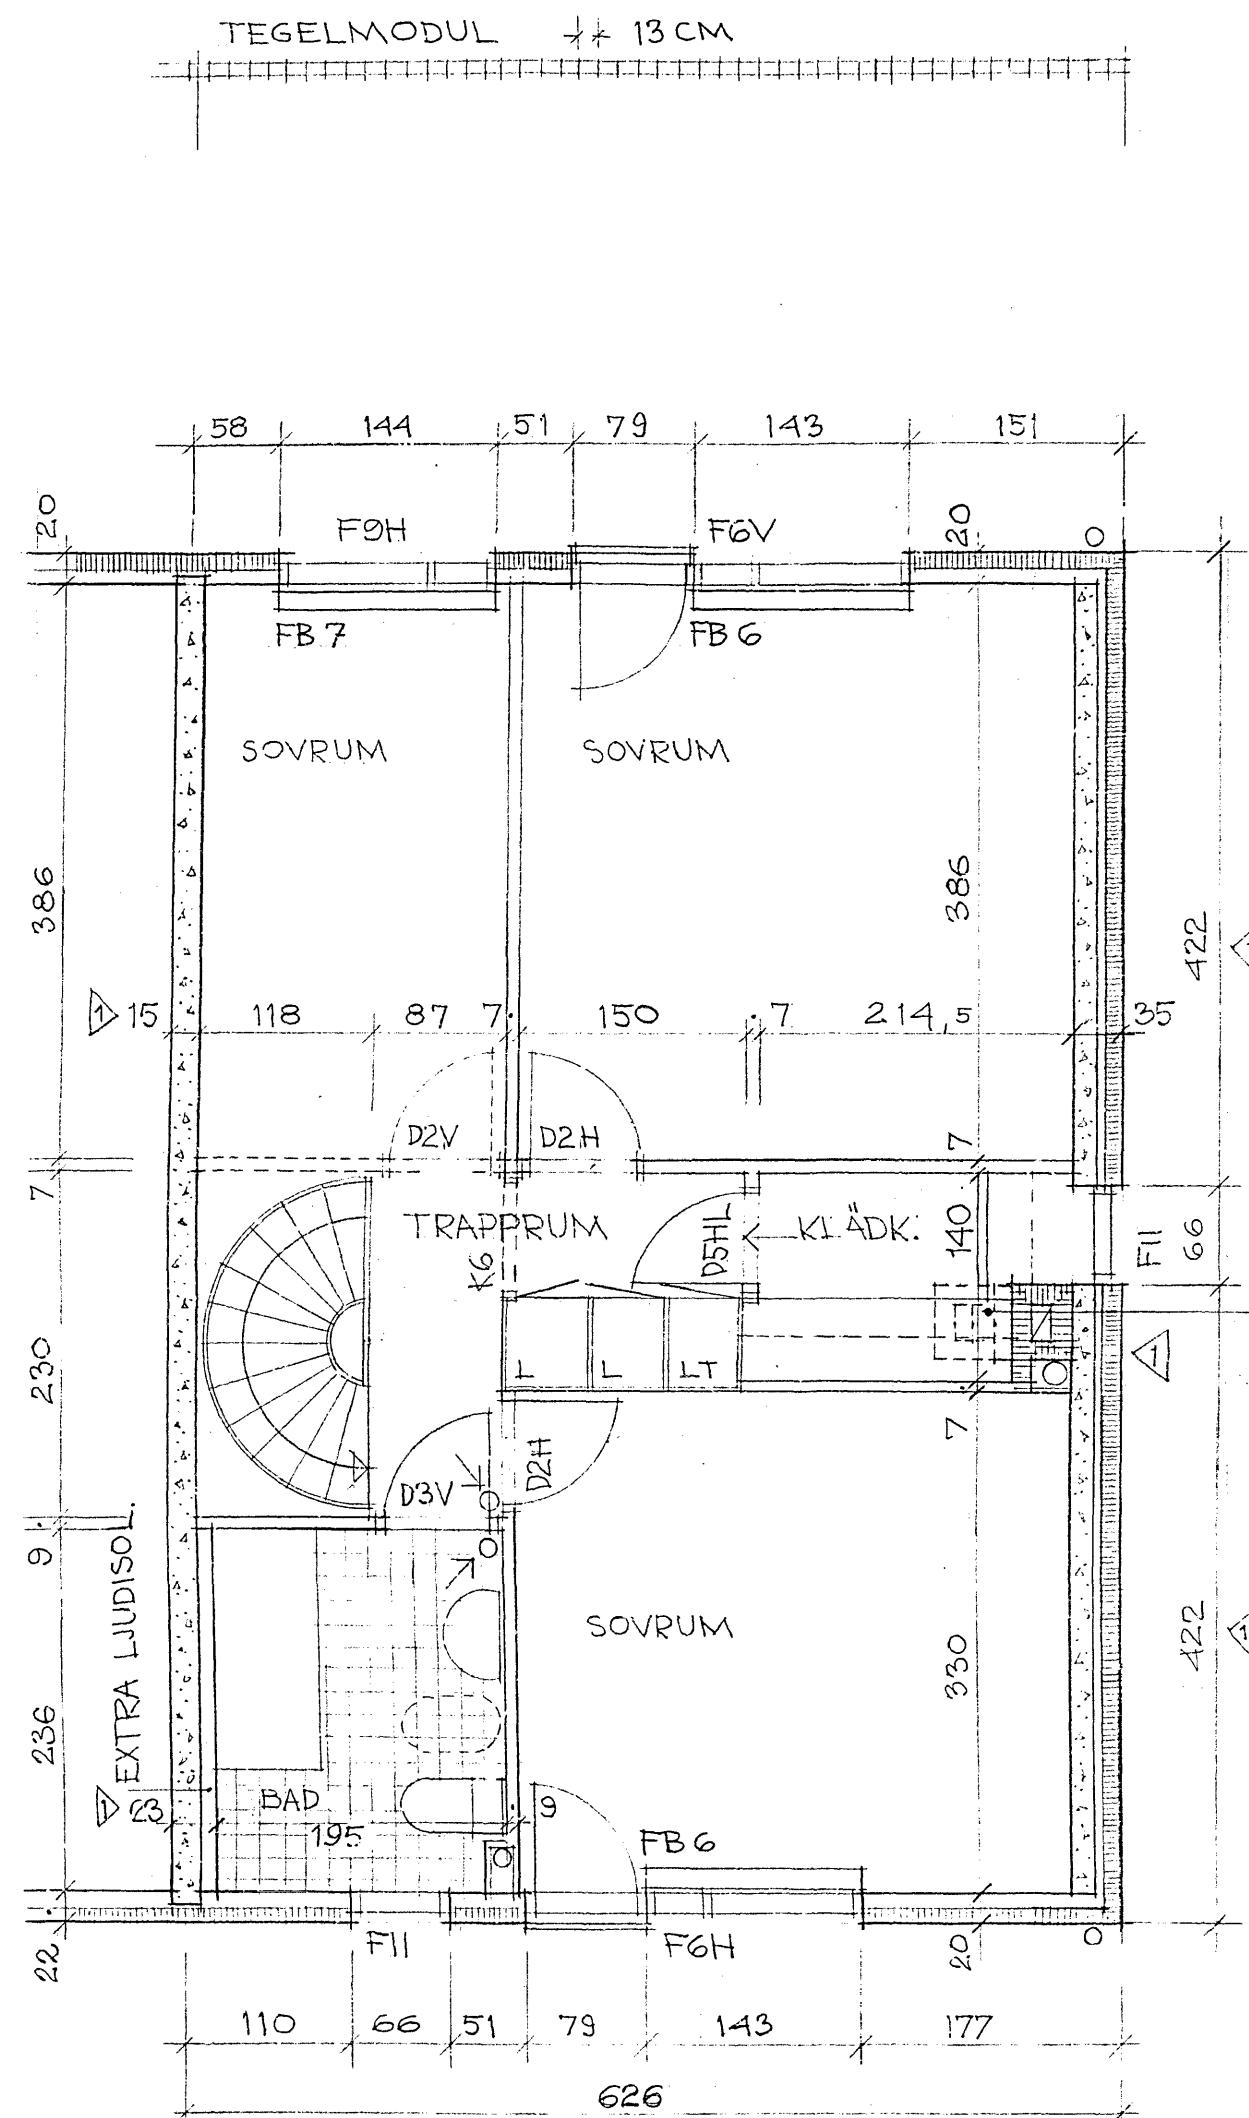

ÖVERPLAN

MÅTT AVSER FÄRDIG VÄGG

TEGEL
BETONG

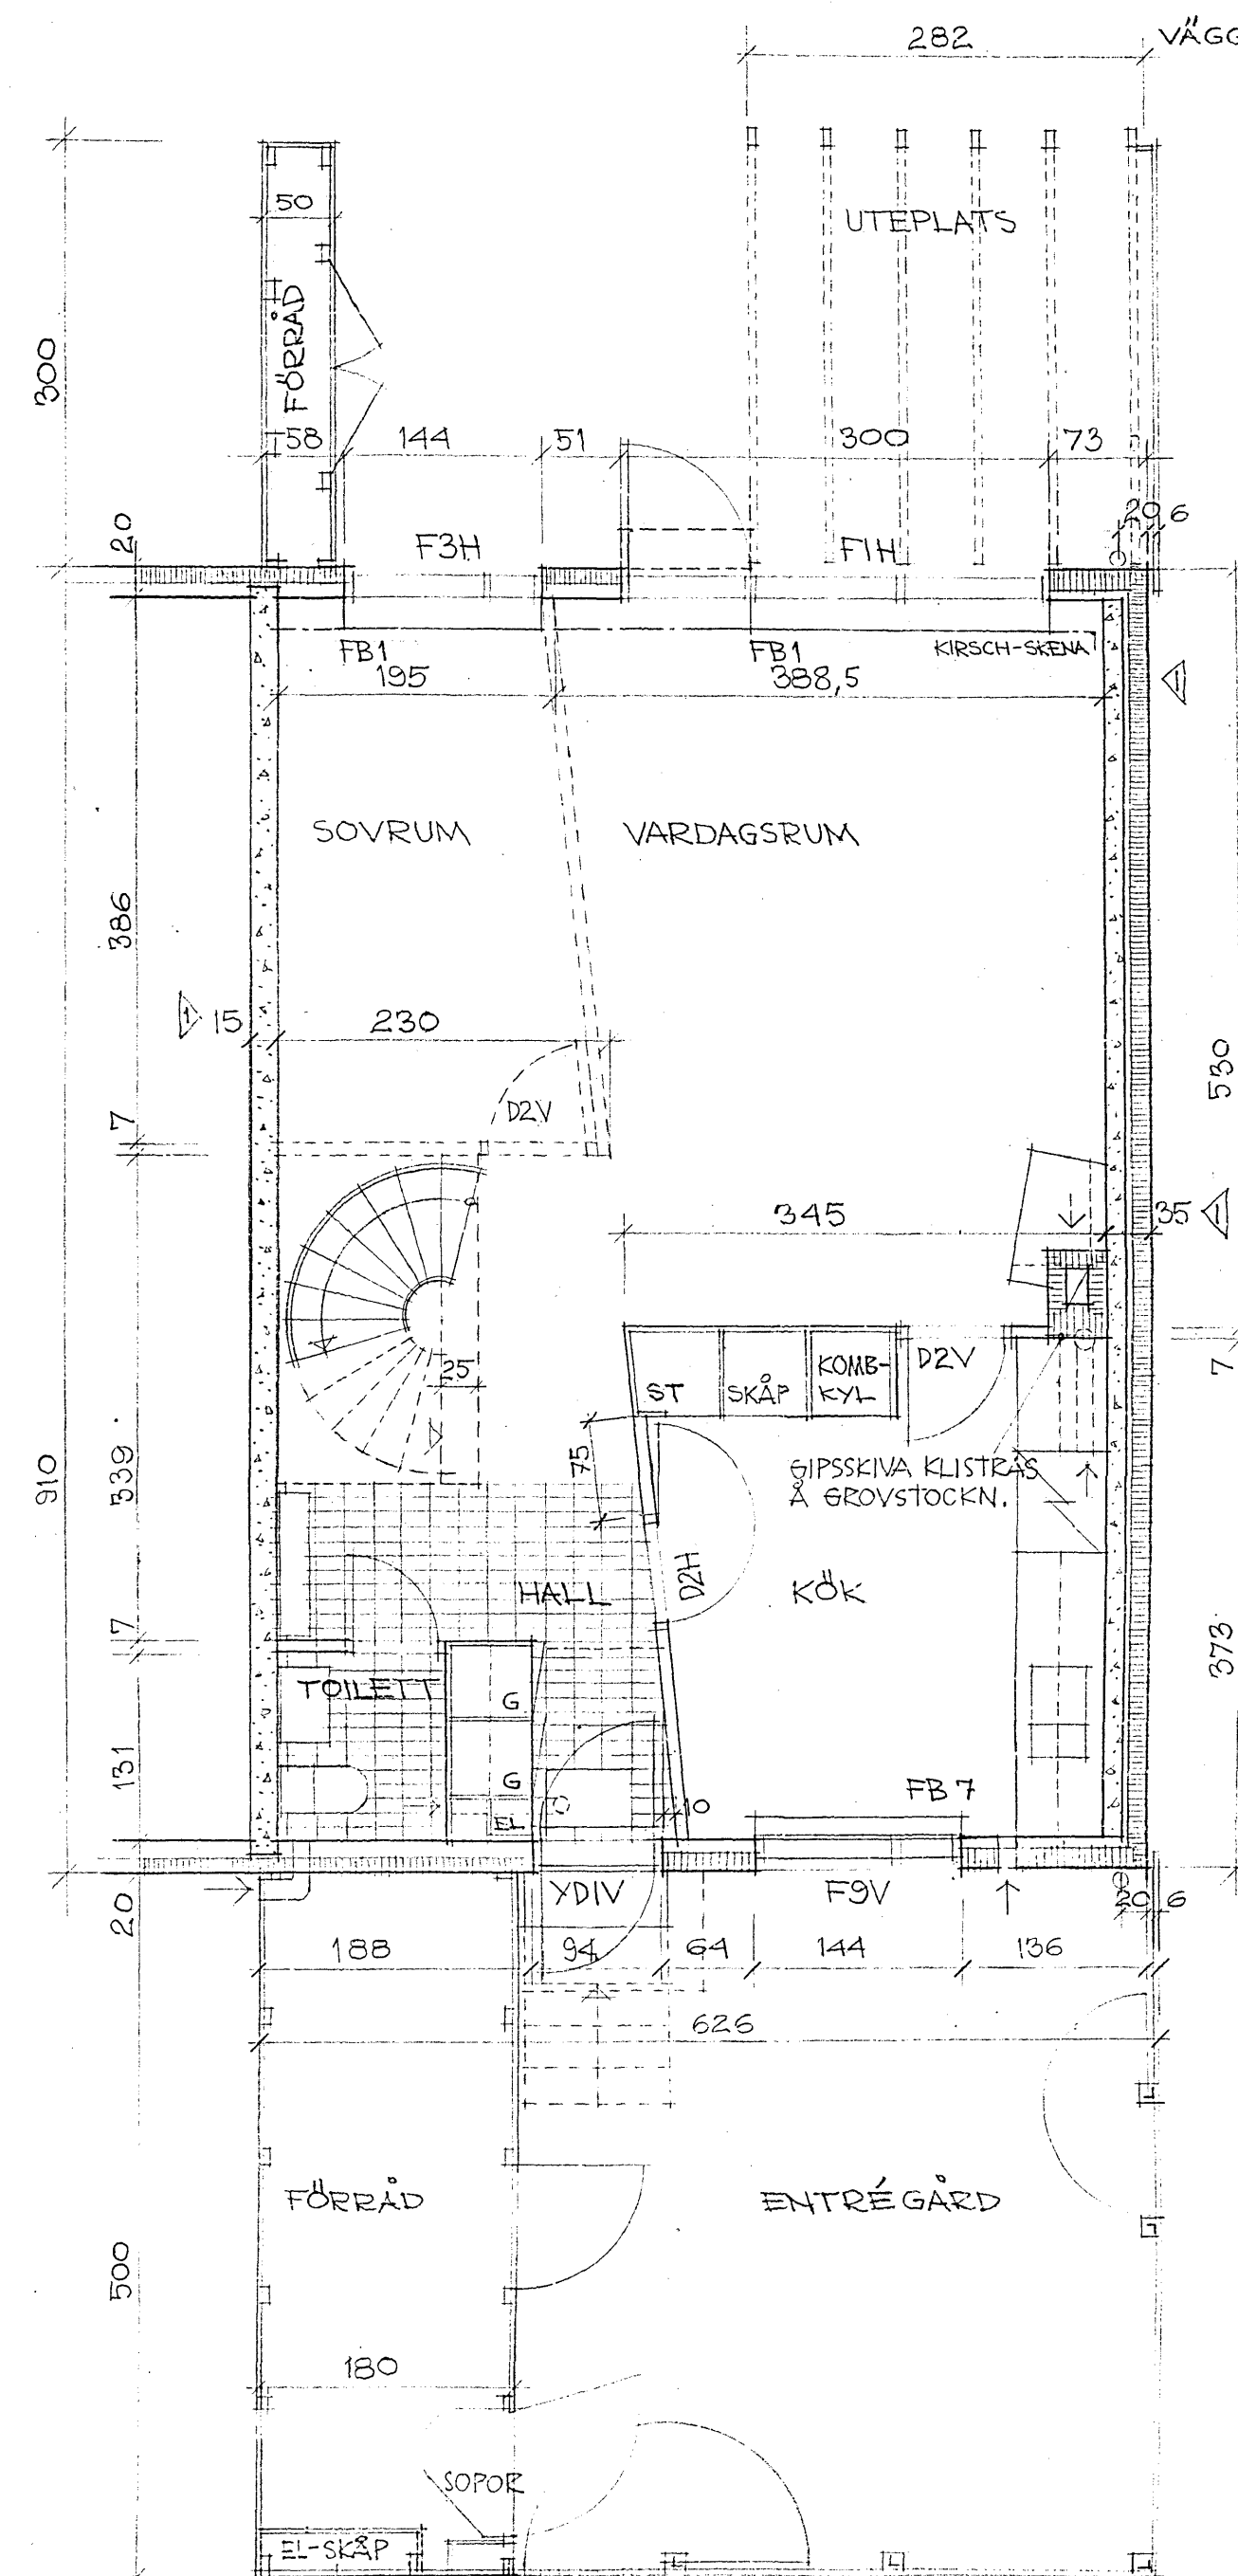

BOTTENPLAN

REV. 26.10.60 SKORSTEN, BJE, MÅTT, VENT.
REV. 21.9.60 FRIGOLIT UTEÅR I KÖK.
REV. 19.8.60 MÅTT 385,5, 151
REV. 15.8.60 SKORSTEN
REV. 27.6.60 IMKANAL

ROBERTSHÖJD
GÖTEBORGS STADS BOSTADSBOLAG
5 RUM OCH KÖK

ARKITEKTERNA
POUL HULTBERG OCH ARNE NYGÅRD SAR
V. HÄRNO. 24-26, GÖTEBORG C, TEL. 106032, 106042

ARB. NR 5811
BLOCK 26-23
TYP BAS
SKALA 1:50
JEN 15.6.60
RITN. NR 102